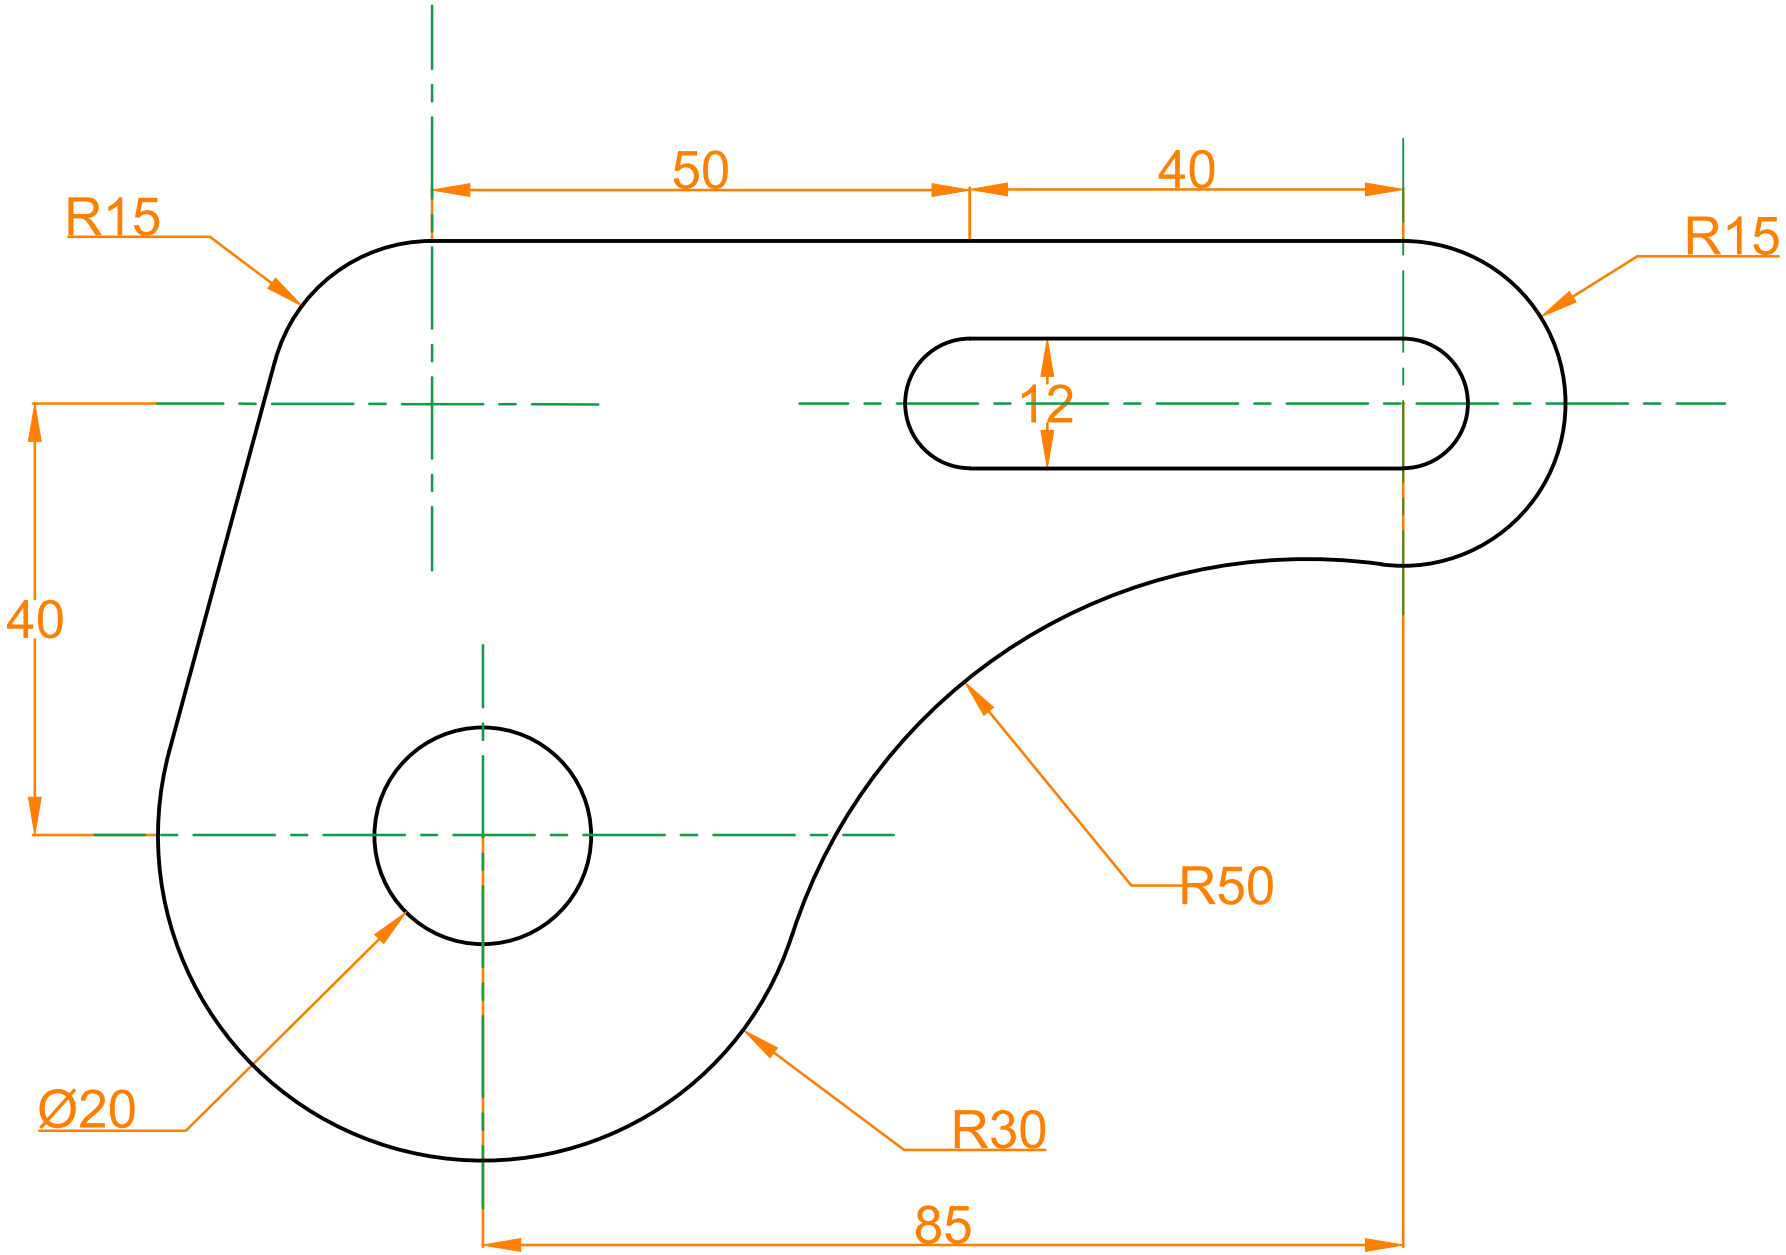

50
40
R15
R15
12
40
R50
Ø20
R30
85